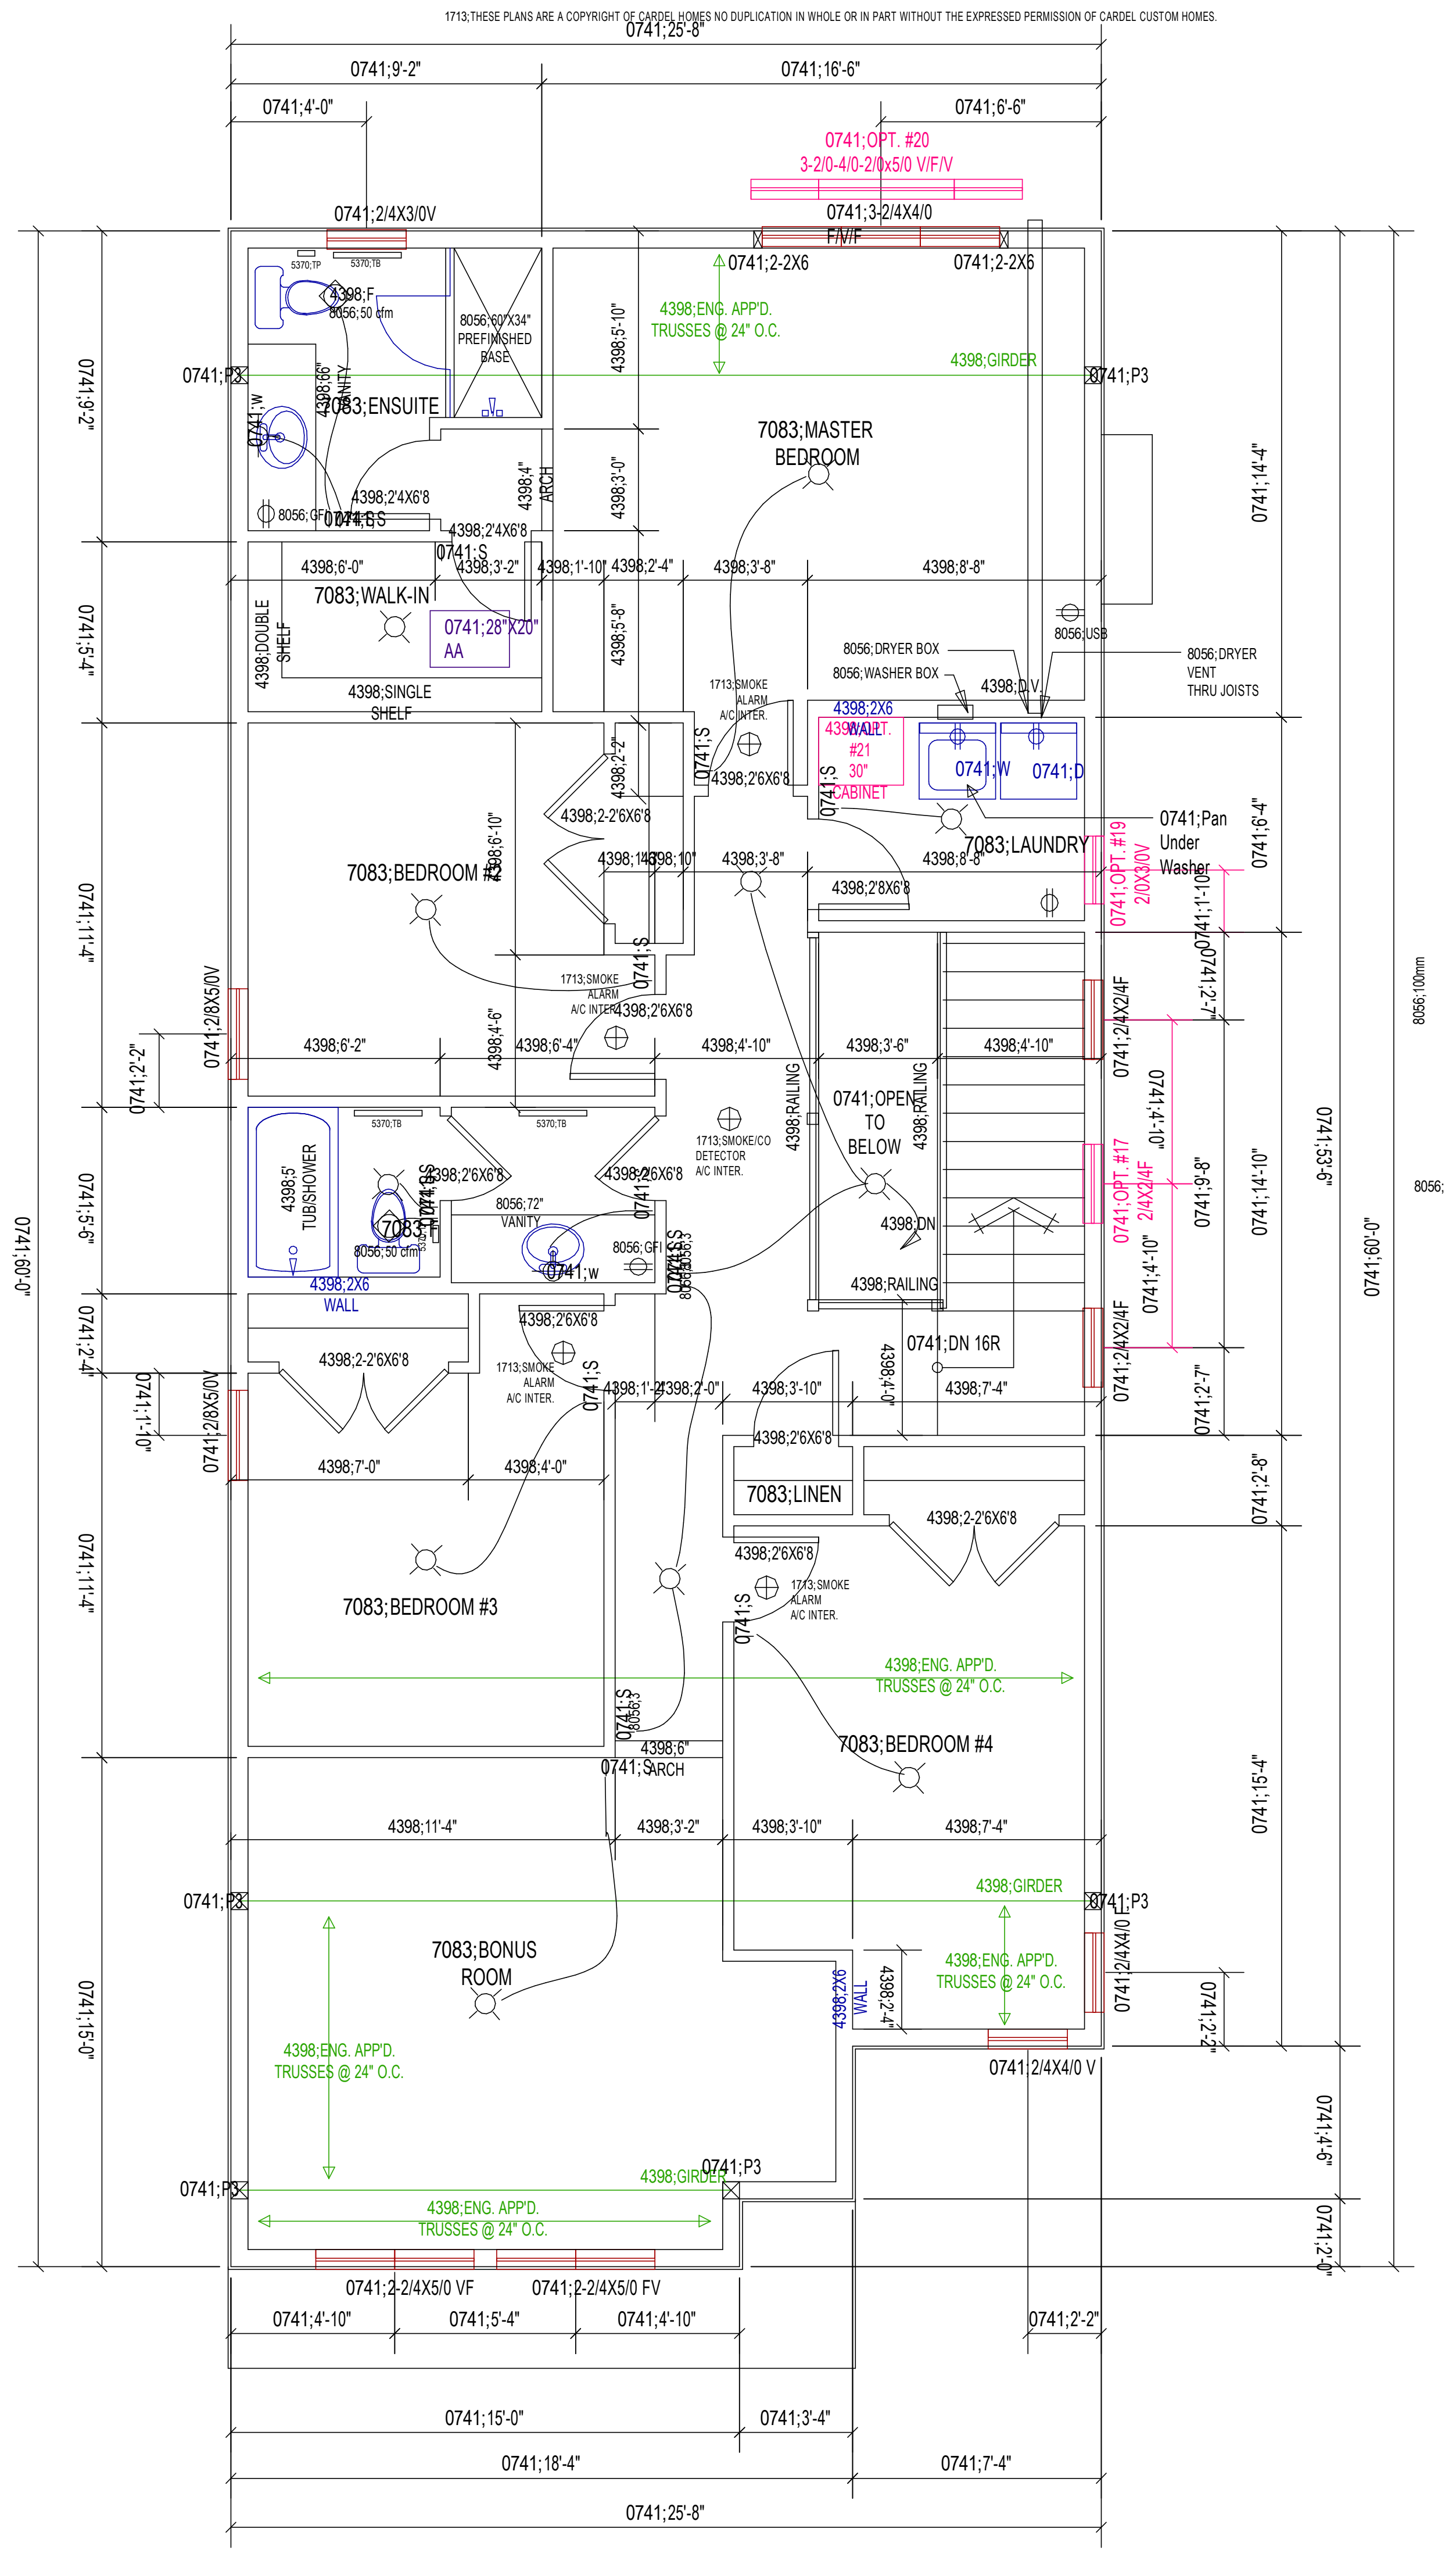

3 03 Upper Floor Plan_Linked Cad files

1 : 60

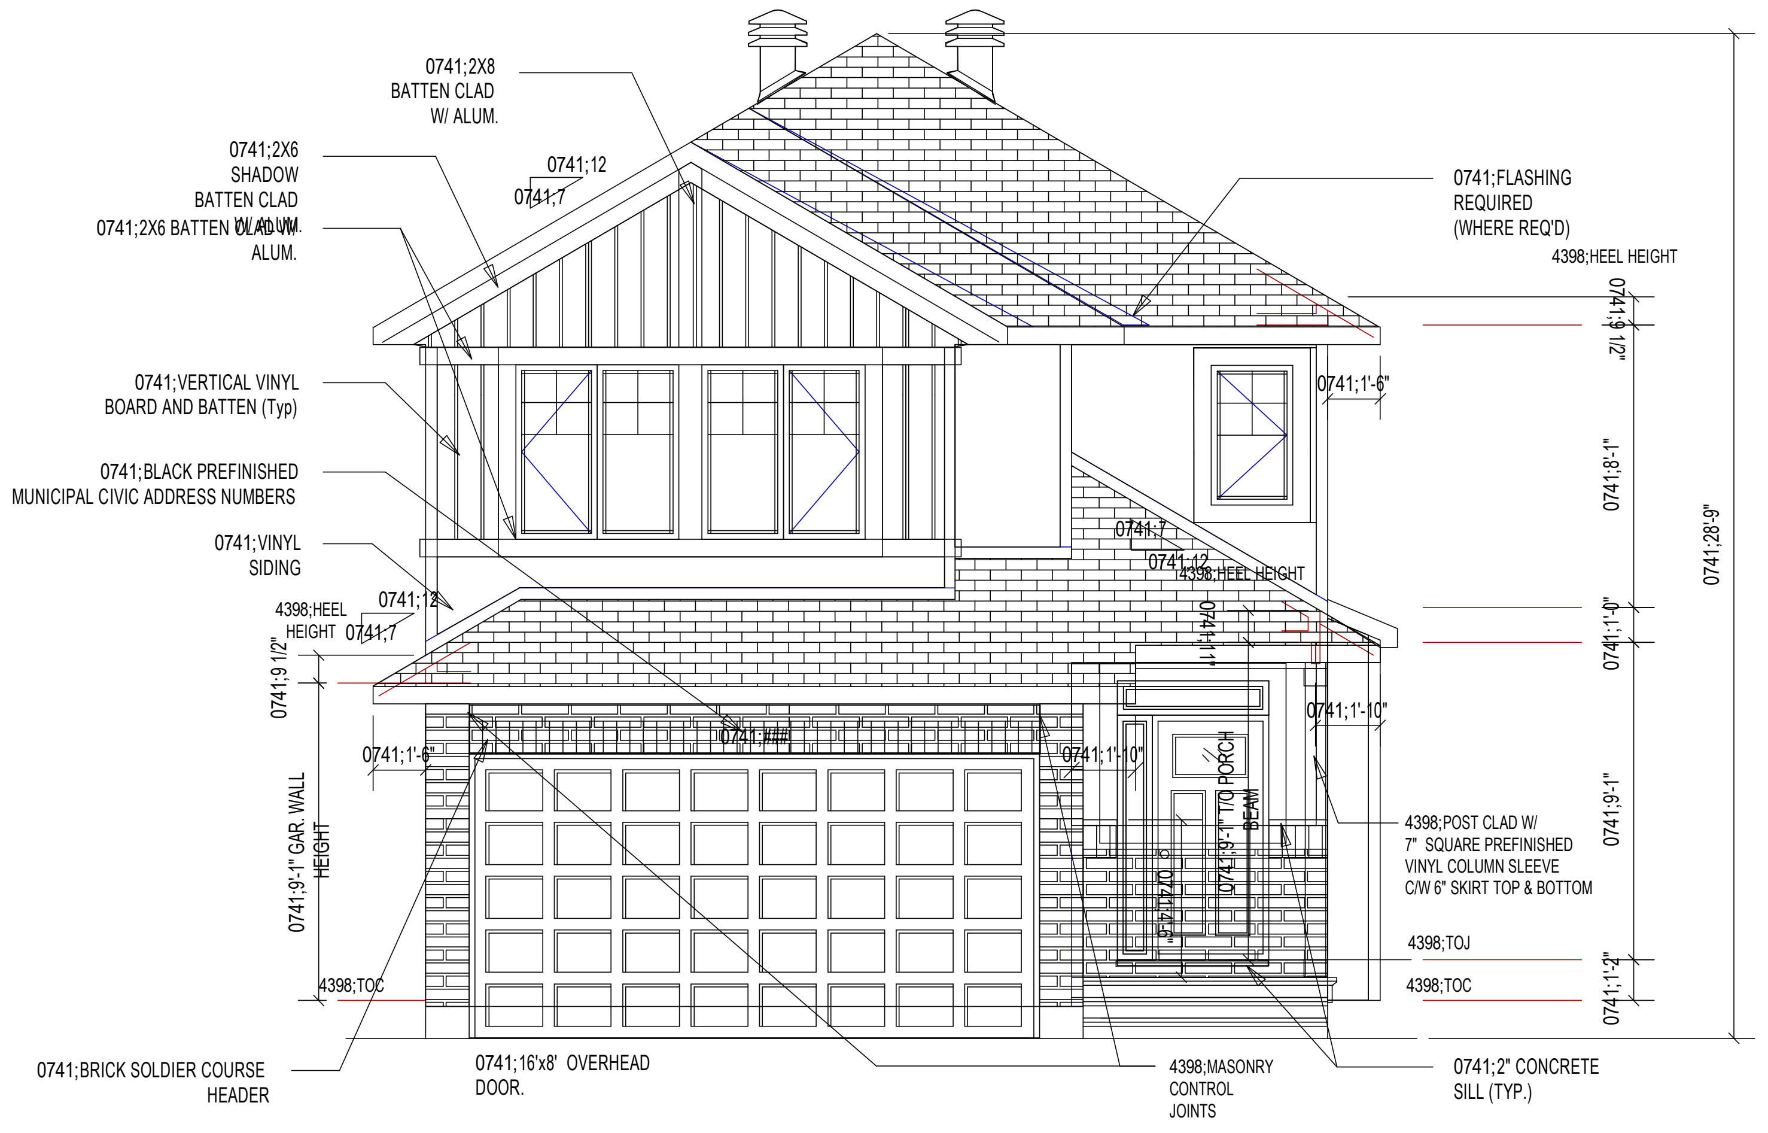
0741;2X8 BATTEN CLAD W/ ALUM.
0741;2X6 SHADOW BATTEN CLAD W/ ALUM.
0741;12
0741;7
0741;FLASHING REQUIRED (WHERE REQ'D)
4398;HEEL HEIGHT
0741;VERTICAL VINYL BOARD AND BATTEN (Typ)
0741;BLACK PREFINISHED MUNICIPAL CIVIC ADDRESS NUMBERS
0741;VINYL SIDING
4398;POST CLAD W/ 7" SQUARE PREFINISHED VINYL COLUMN SLEEVE C/W 6" SKIRT TOP & BOTTOM
4398;TOJ
4398;TOC
0741;BRICK SOLDIER COURSE HEADER
0741;16'x8' OVERHEAD DOOR.
4398;MASONRY CONTROL JOINTS
0741;2" CONCRETE SILL (TYP.)
0741;28'-9"

04 04 Front Elevation_Linked Cad files

1 : 60

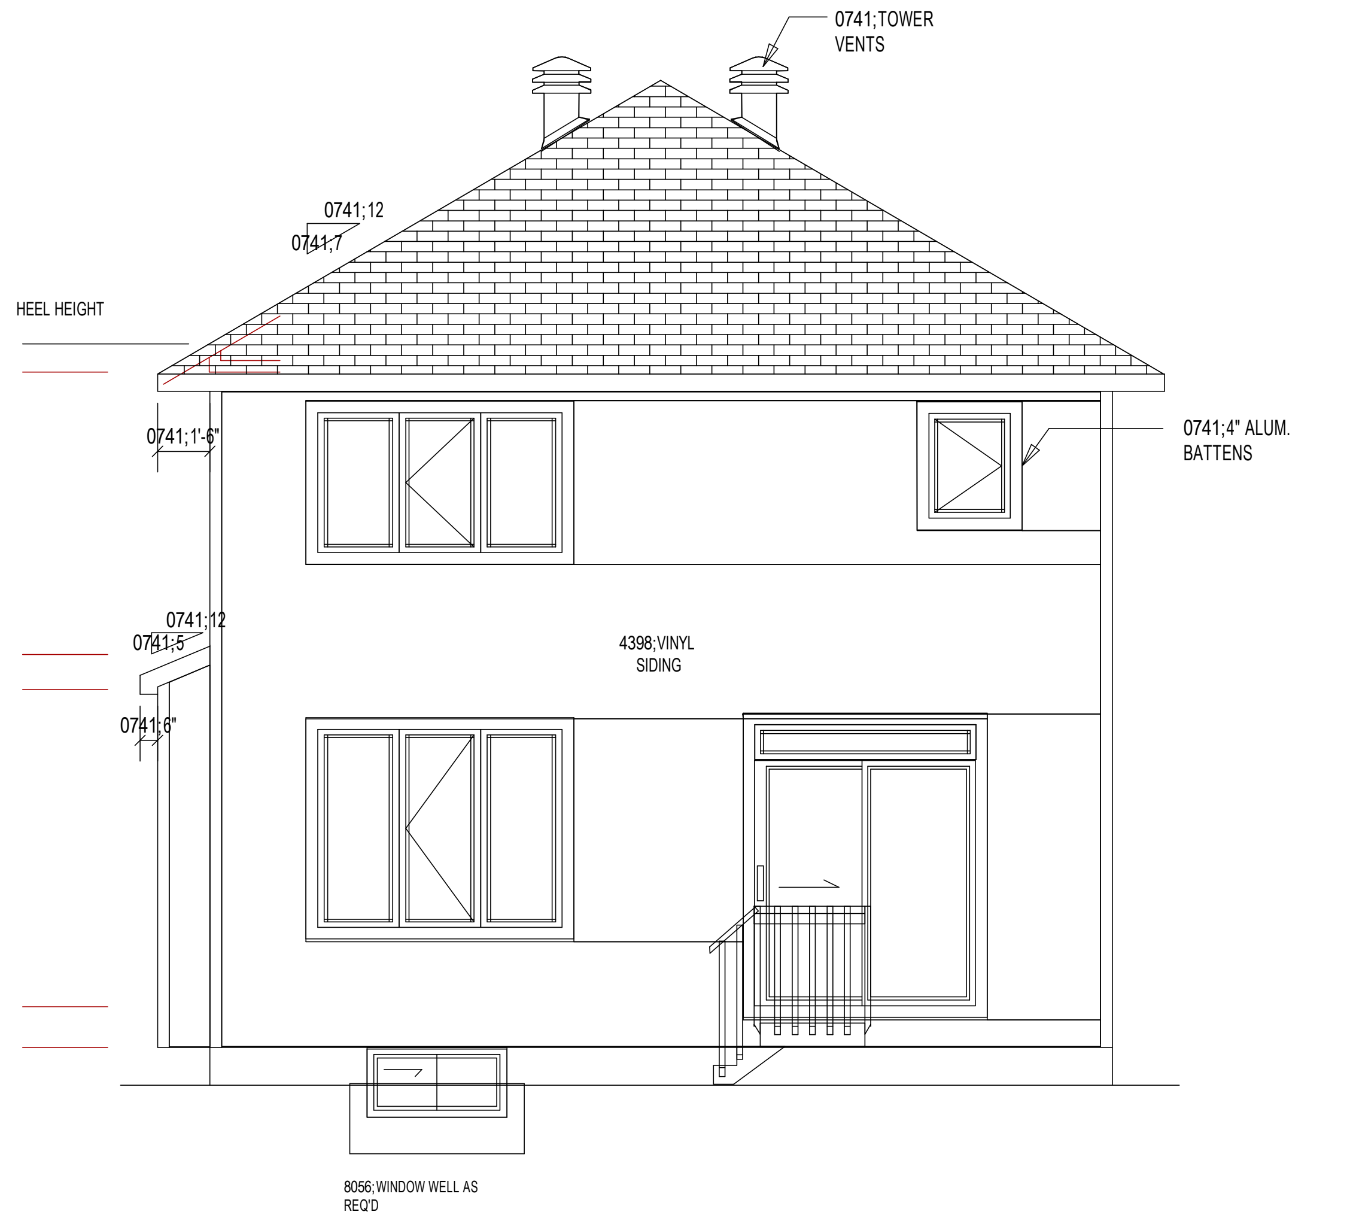

05 05 Rear Elevation_Linked Cad files

1 : 60

SCHOOL: LOCATION:	**ALGONQUIN COLLEGE** **1385 Woodroffe Ave Ottawa, Ontario K2G 1V8**	SUBJECT: DEADLINE:	**IMPORTING CAD – CARDEL HOME: PLANS (2), ELEVATION (4), SECTION (1)** **2023-02-20**	SHEET NAME:	**UPPER-LEVEL PLAN, FRONT ELEVATION & REAR ELEVATION**	PAGE NO.: **7**
COURSE NAME: PROFESSOR:	**23W BIM1011_310_BIM FUNDAMENTAL 1** **AR. NICOLAS ARELLANO_Ph.D.**	DRAWN: DATE:	**KIM ZF MAGNAYE** **2023-04-06 12:15:17 PM**	SHEET NO.:	**AL-W23-BIM-1011-ASS-05-02**	

C:\Users\KIM\Documents\BIM1011-W23.KIMZF.MAGNAYE_magn0045.rvt